

PORTFOLIO


TAUTVYDAS GRIGALASKAS

SELECTED ARCHITECTURE · 2024-2025

CONTENTS

01. JOCHY TOWER PROJECT PROPOSAL	03
02. SEMEY MALL PROJECT PROPOSAL	07
03. ETERNAL PEARLS CONTEST PROPOSAL	10
04. URBAN BLOCK ACADEMIC PROJECT	12

01 JOCHY TOWER


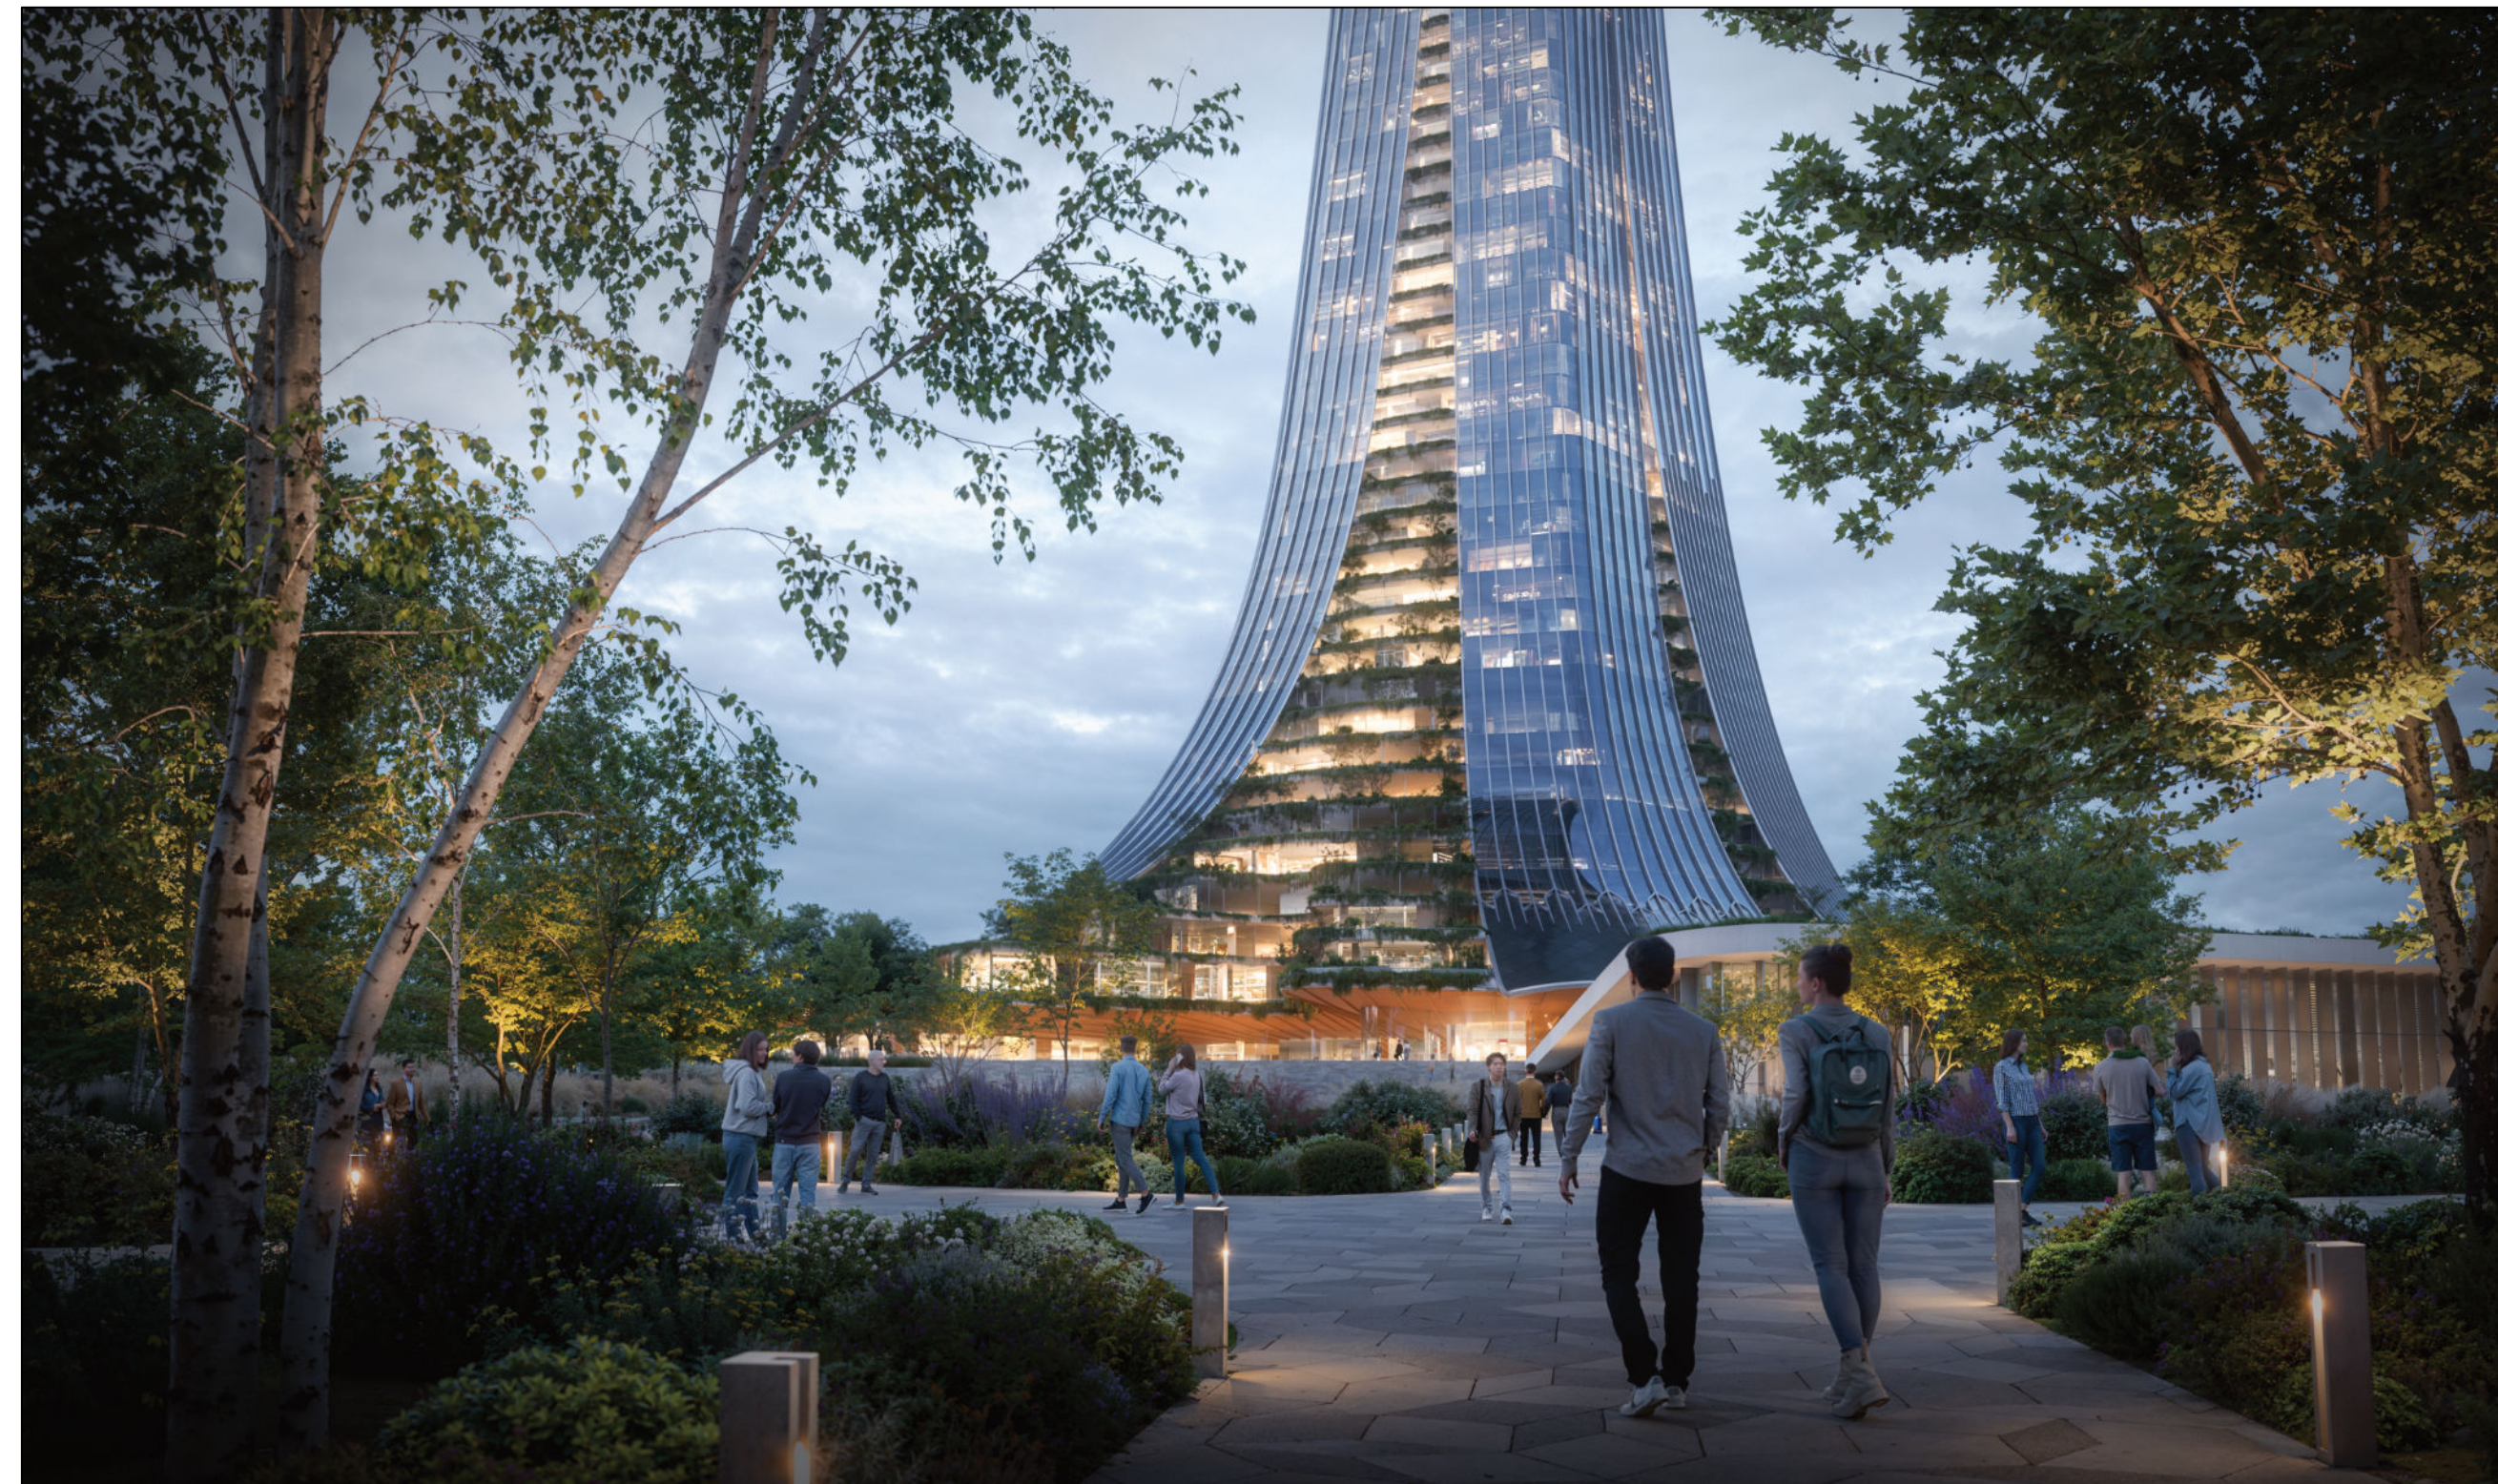


VISION

Jochy Tower is envisioned as a new-generation urban landmark—an architectural statement that simultaneously represents technological progress, cultural identity, and the human connection to nature. The project is not conceived simply as a skyscraper, but as an urban system that shapes a new city center, a network of public spaces, and a new relationship between people, the city, and the landscape.

The tower is located at the point where the dense urban fabric transitions into the open horizon of the steppe. This threshold becomes the project's central theme, with the architecture extending it vertically. The building's form, terraces, greenery, and public spaces interpret the movement of the steppe winds, the flow of the river, and the ever-changing dynamics of the landscape.


Rather than creating an isolated object, the project aims to establish a vibrant urban structure that functions around the clock and becomes a new destination for both residents and visitors.

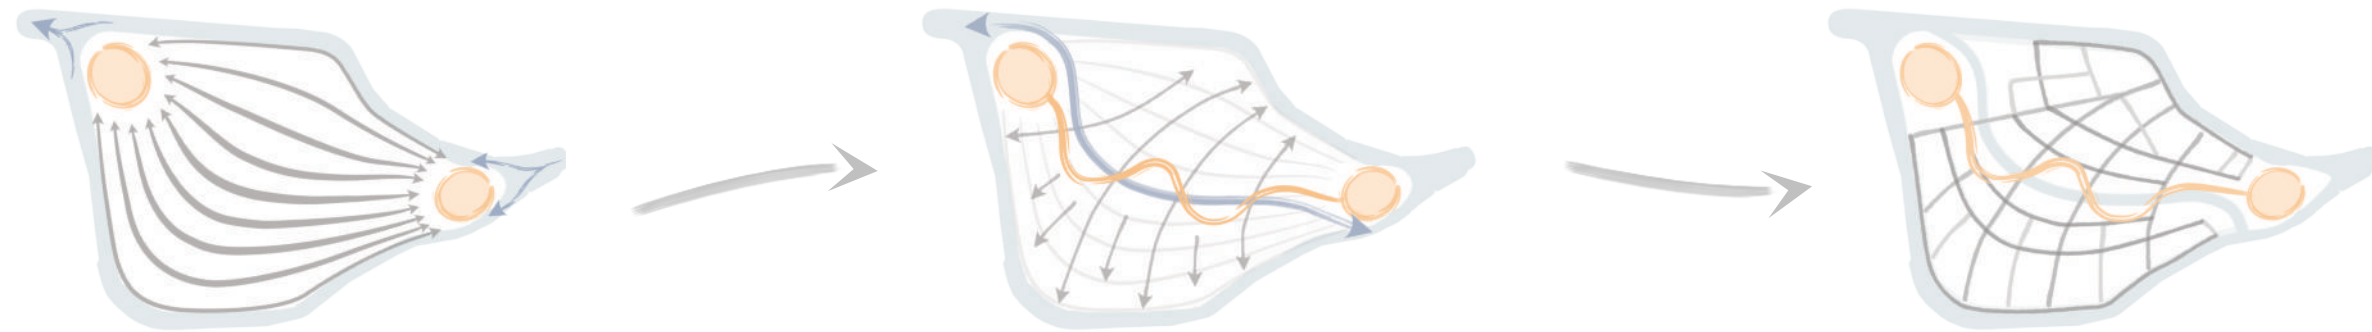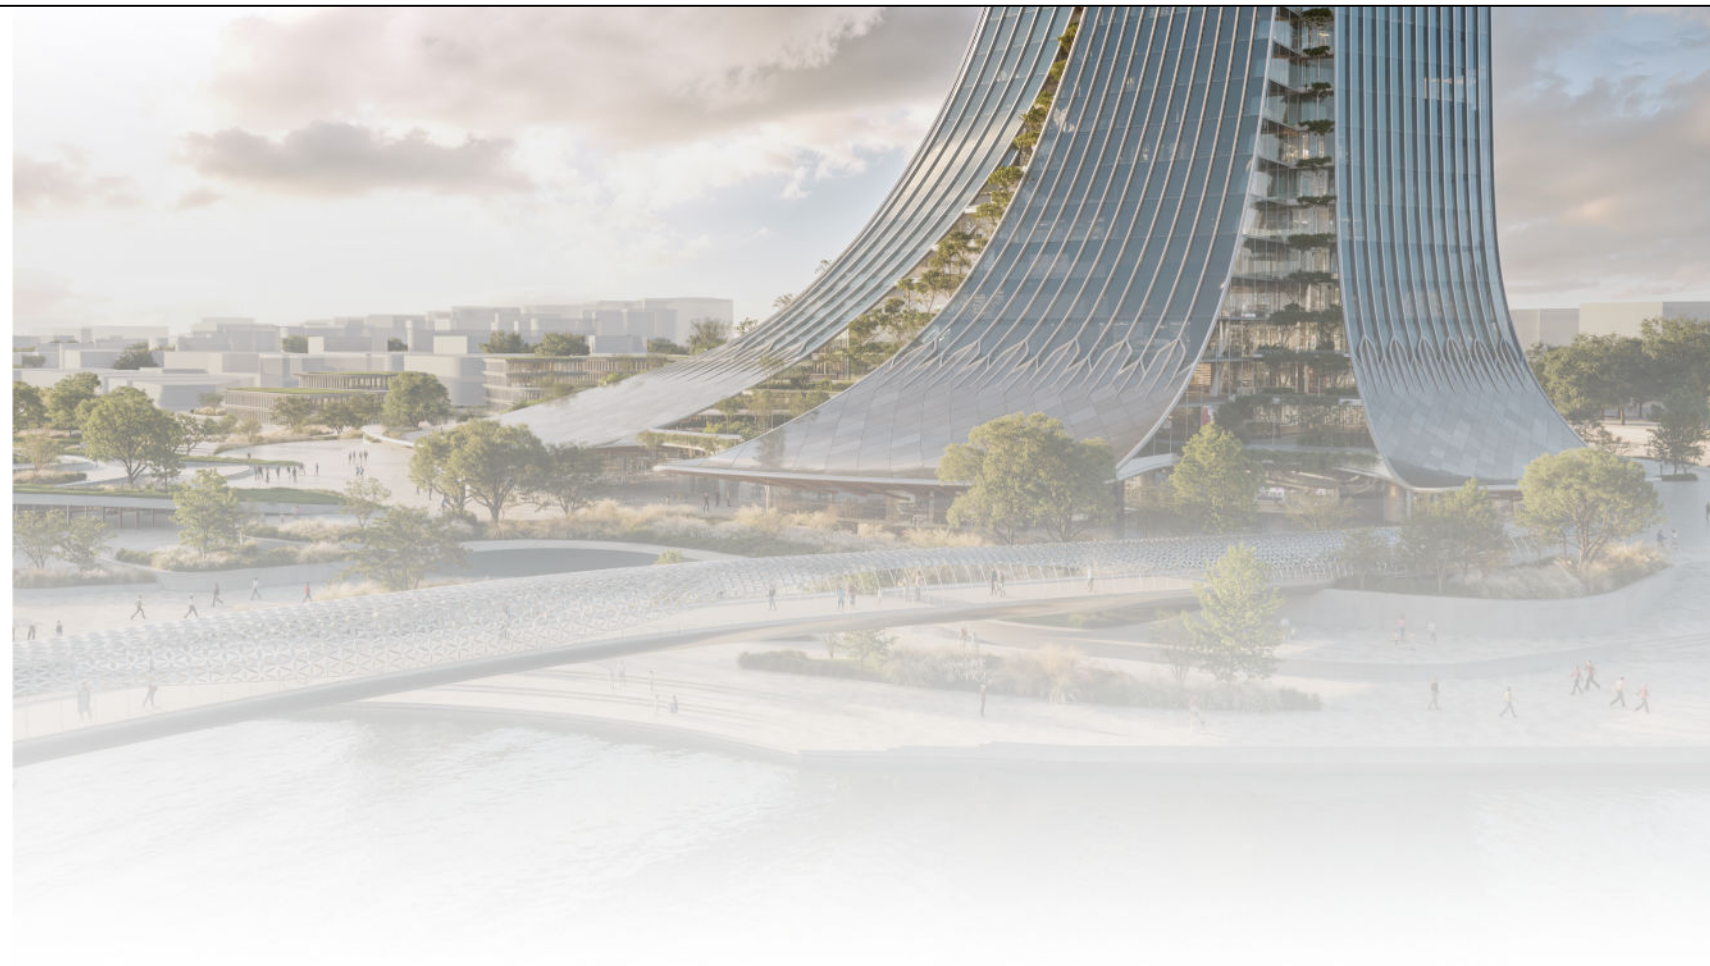

MASTER PLAN

The primary urban design principle is to connect different layers of the city into one continuous network. For this reason, the site is organized not around a single building, but around a system of public spaces positioned at the heart of the development.

A central water axis serves as the main landmark and unifying element. More than simply dividing the site, it creates connections between different functions and destinations. Squares, green spaces, promenades, and pedestrian routes are arranged around the canal, linking the tower with the surrounding urban fabric.

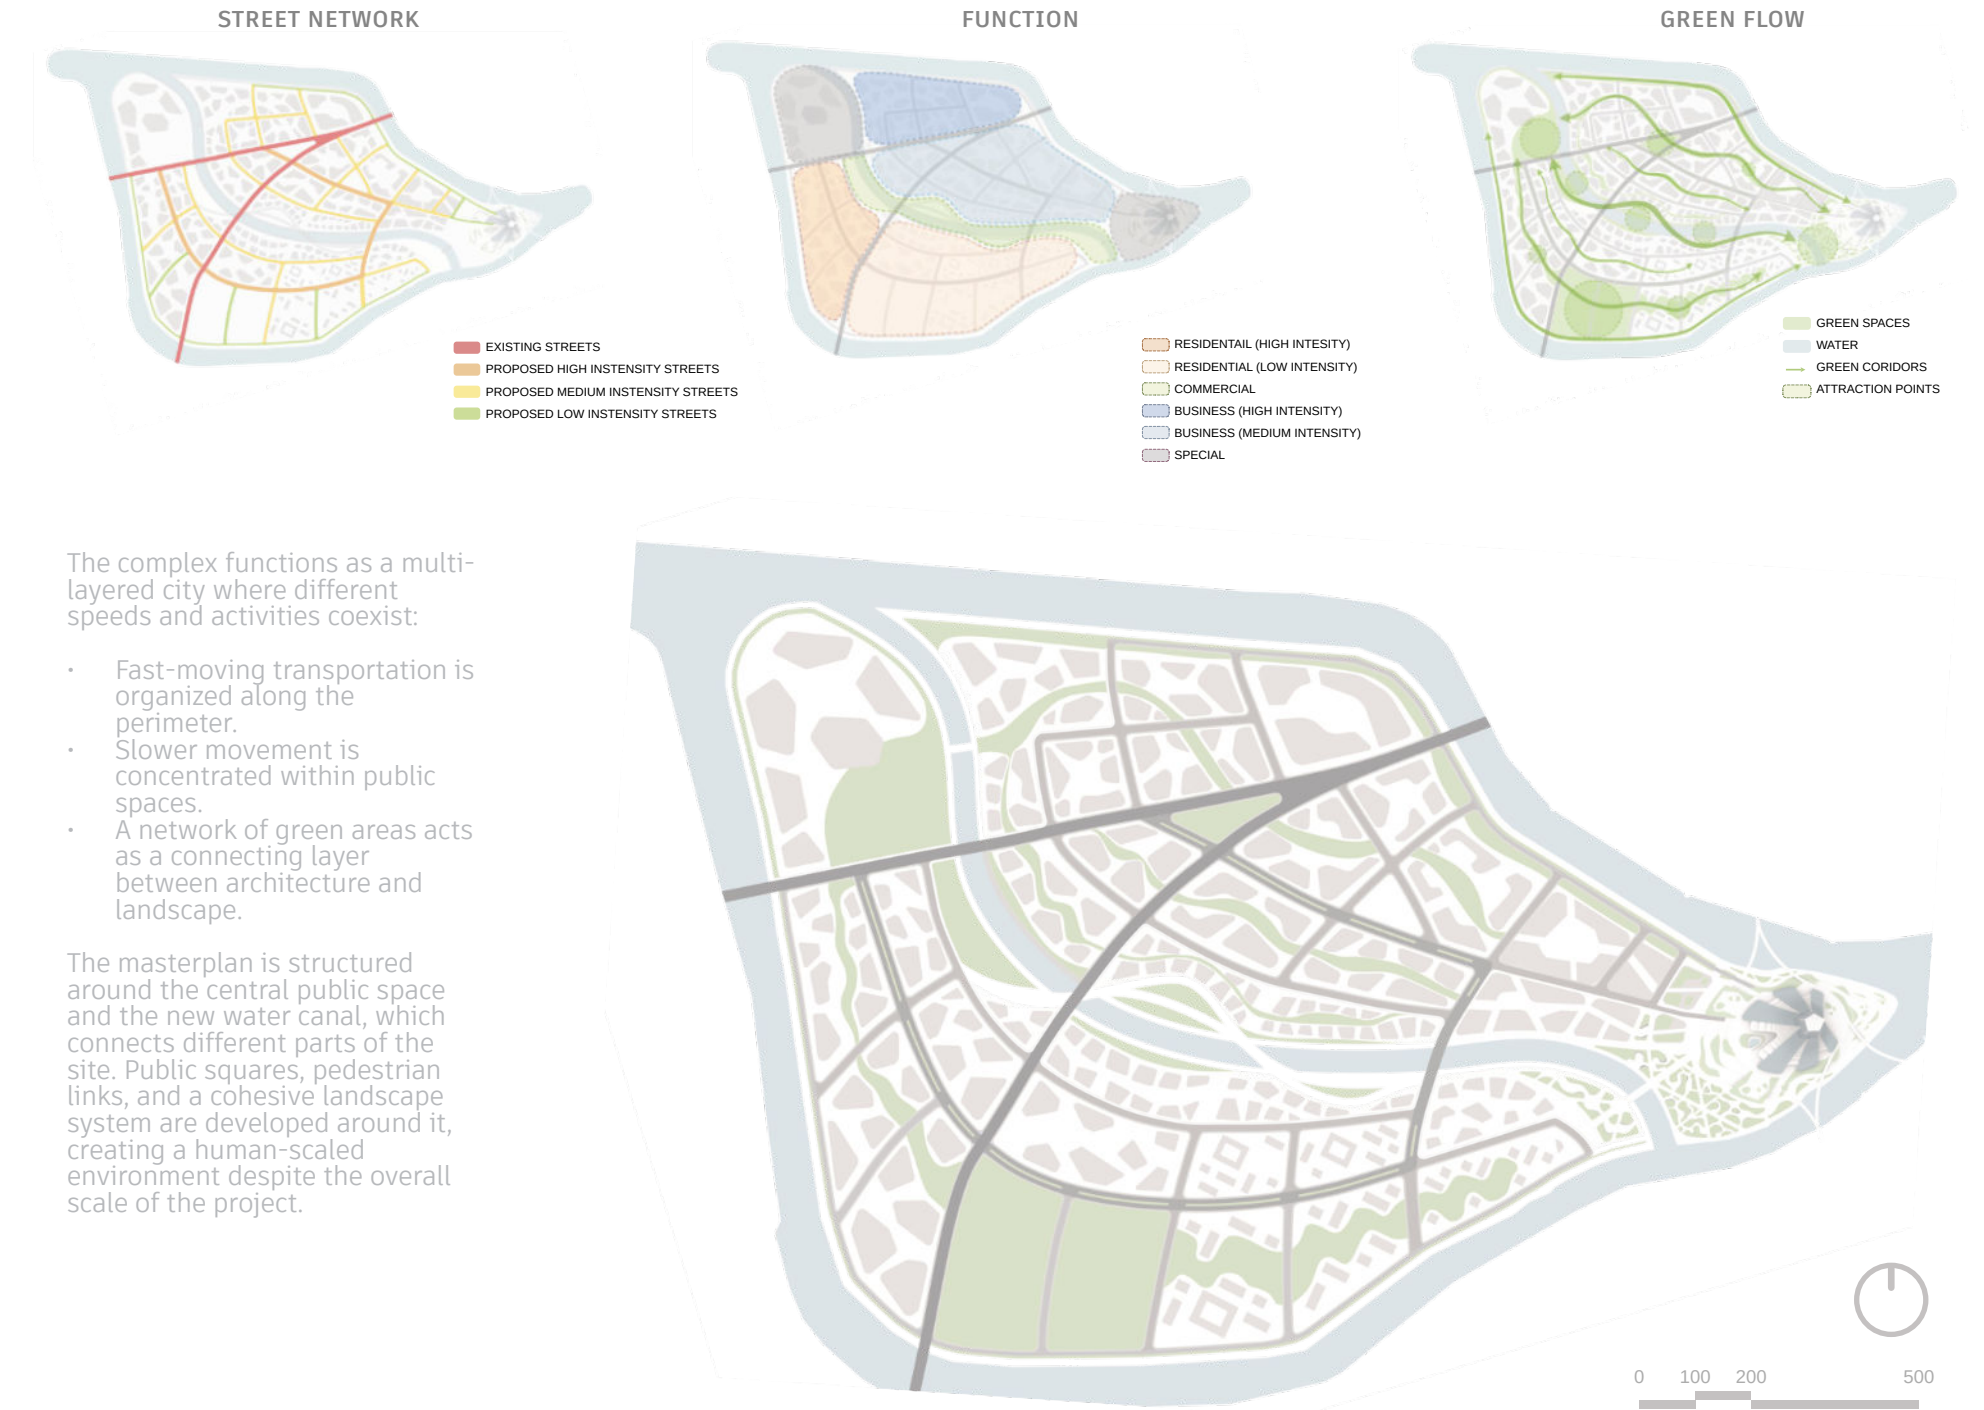

The complex functions as a multi-layered city where different speeds and activities coexist:

- Fast-moving transportation is organized along the perimeter.
- Slower movement is concentrated within public spaces.
- A network of green areas acts as a connecting layer between architecture and landscape.

The masterplan is structured around the central public space and the new water canal, which connects different parts of the site. Public squares, pedestrian links, and a cohesive landscape system are developed around it, creating a human-scaled environment despite the overall scale of the project.




SITE PLAN


The project aims to bring the scale of high-rise architecture closer to people. To achieve this, the development gradually increases in density and height, while public spaces remain human-scaled and pedestrian movement is prioritized throughout the site.

The project is located along the riverfront, where the urban fabric meets an open natural landscape. This transition becomes a key urban design element, shaping the overall structure of the development.

Building heights are carefully arranged to create a smooth transition between the denser urban core and the surrounding public spaces, helping to integrate the tower into its wider context.

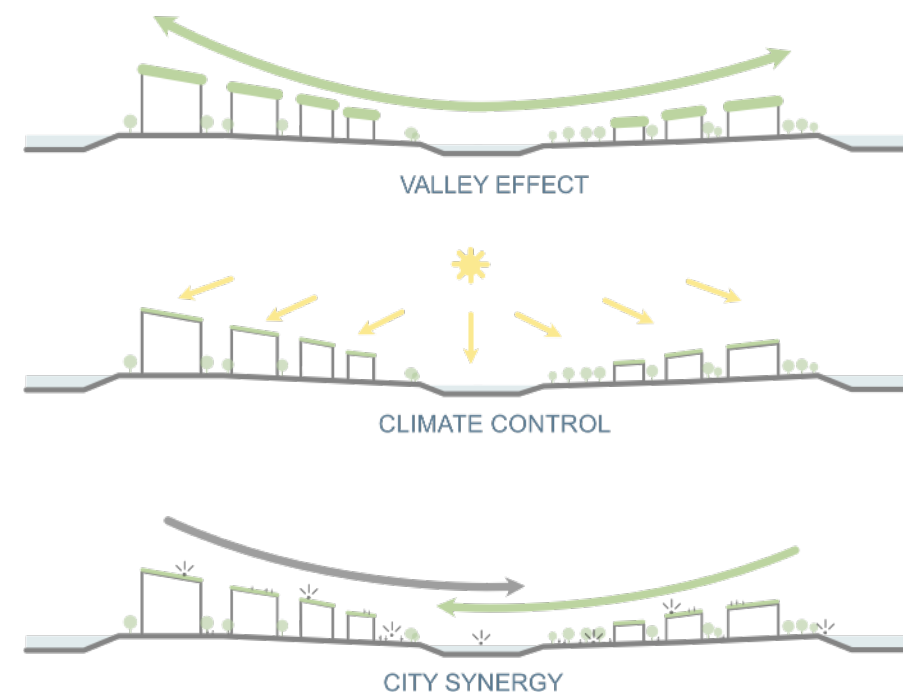

ARCHITECTURAL CONCEPT

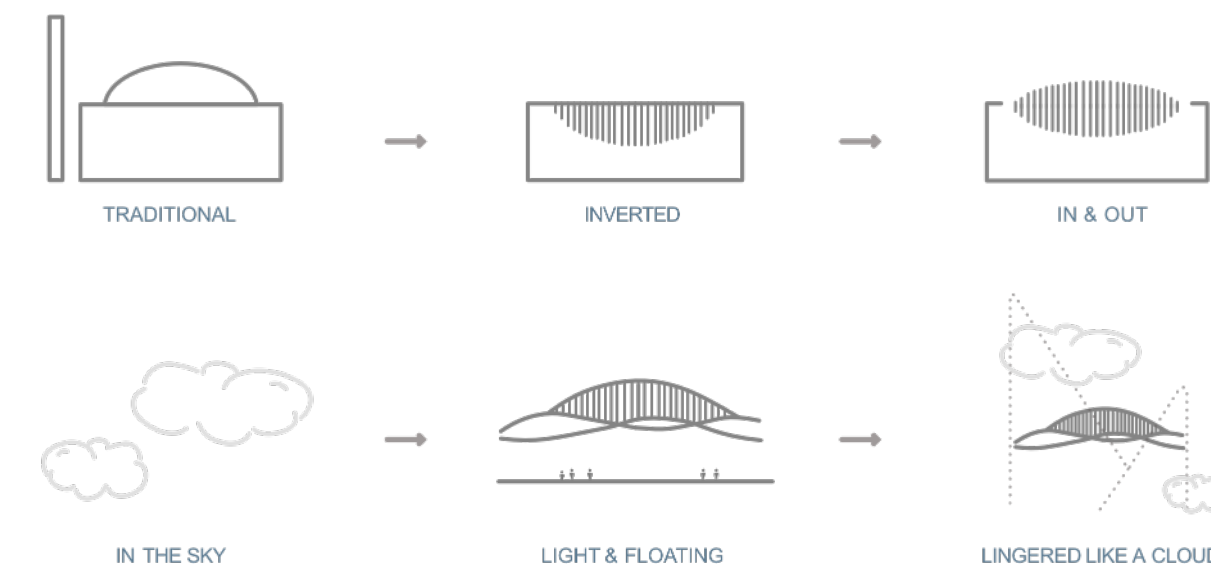

Podium


The podium naturally extends the tower, creating fluid and organic spaces that connect nature, the city, and people. Landscaped terraces and open balconies provide expansive views, while interconnected spaces encourage movement and social interaction. Pathways and forms unfold across multiple levels, inviting exploration and allowing the architecture to blend seamlessly with its surroundings..

Tower


The glass-clad tower rises as a symbol of urban growth and progress. It brings together offices, a hotel, and residential spaces, creating a destination where work, leisure, and everyday life coexist. Panoramic views open up from the upper levels, while the connection to the podium remains clear and continuous. The tower reflects the energy and dynamism of a contemporary city.

Crown


At the top of the tower are a mosque and the “Seven Heavenly Gardens.” This space is dedicated to prayer, reflection, and tranquility. Its design draws inspiration from geometry and nature, creating a peaceful environment where architecture and spiritual experience come together.

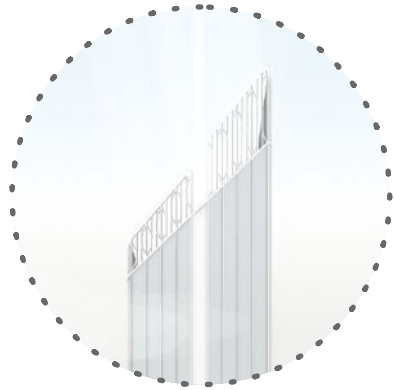


Crown

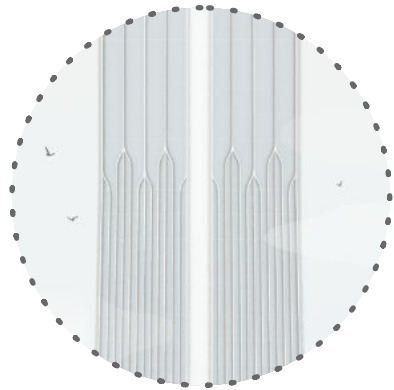

Tower

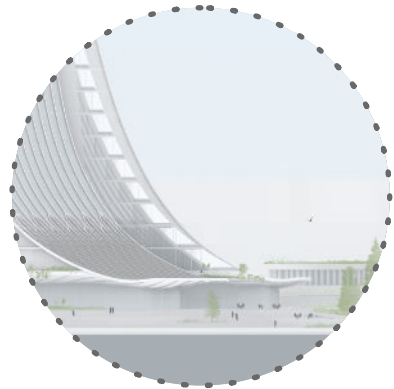

Podium

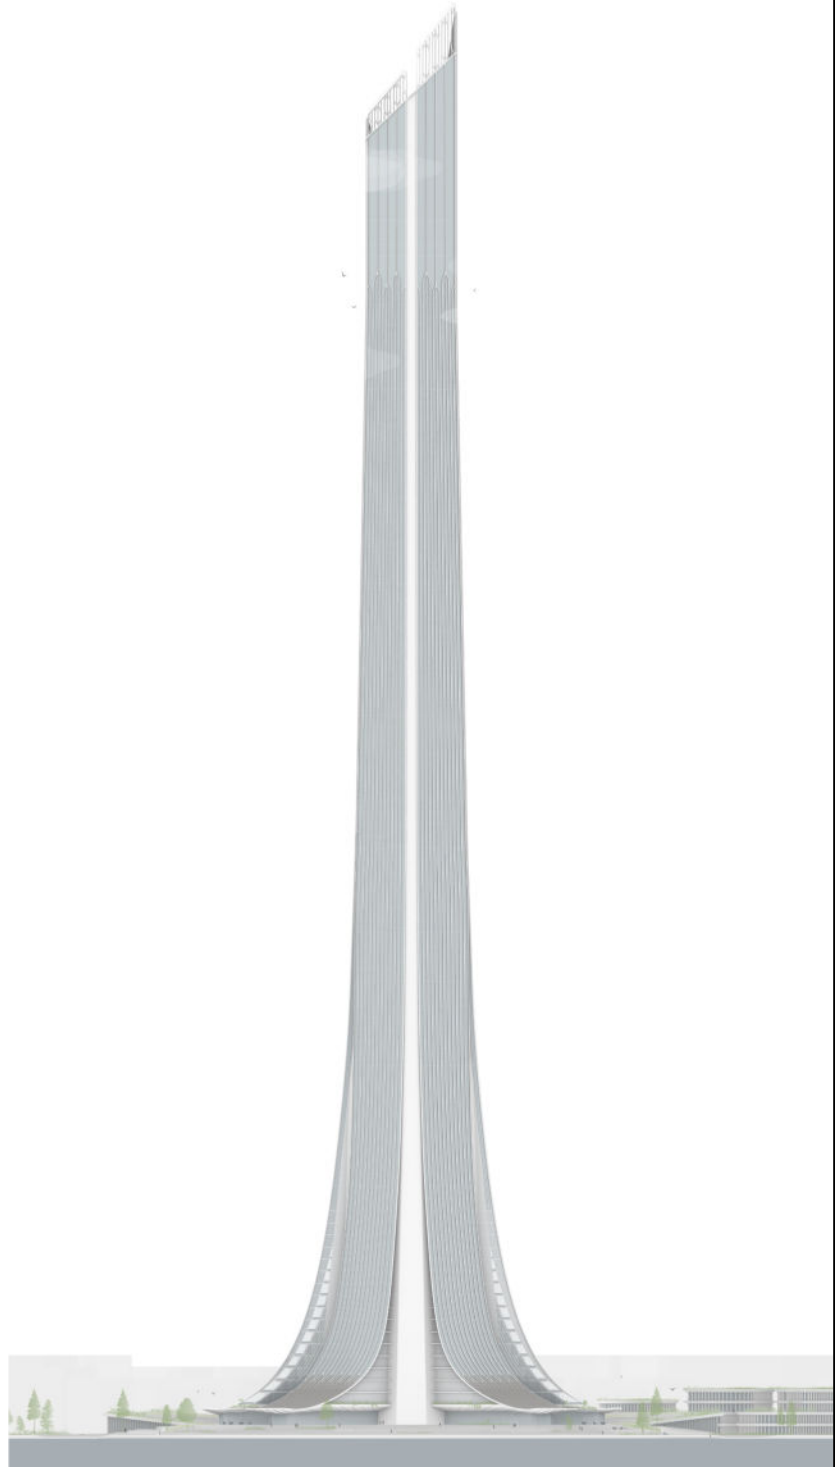

FUNCTION

The building’s form is shaped by key elements of the site’s urban concept, including the extension of development patterns and street axes, as well as forms inspired by river deltas. The tower’s wings are connected by pedestrian bridges that link both the building and the new district to the wider city.

The development accommodates a mix of commercial, office, hospitality, and residential functions. At its center is a primary structural core that gradually tapers as it rises, enhancing the building’s stability. This core contains elevators, staircases, and essential building services.

The project is organized as a vertical city, with different functions layered throughout the structure:

The podium accommodates active public and commercial spaces. The middle section integrates offices, hotel facilities, and residential uses. The upper levels are dedicated to public and spiritual functions.

The podium acts as an extension of the city, connecting public squares, terraces, and key pedestrian routes. Rising above it, the tower becomes a clear landmark visible from across the city.

At the summit, the mosque and the sky gardens create a place of calm above the intensity of urban life below. Their light, almost cloud-like form contrasts with the tower’s rational structure, creating a distinctive architectural climax and defining the identity of the project.

Public

Residential


Hotel

Offices

Commercial

- Commercial area: ~64 900 m²
- Offices area: ~80 900 m²
- Hotel area: ~19 800 m²
- Residential area: ~22 750 m²
- Public (Mosque & Gardens): ~4 550 m²

Total area: ~213 500 m²
Usable area: ~192 900 m²
Core area: ~20 600 m²
Tower area: ~148 600 m²
Podium area: ~64 900 m²
Ground fl. Area: ~ 12 160 m²

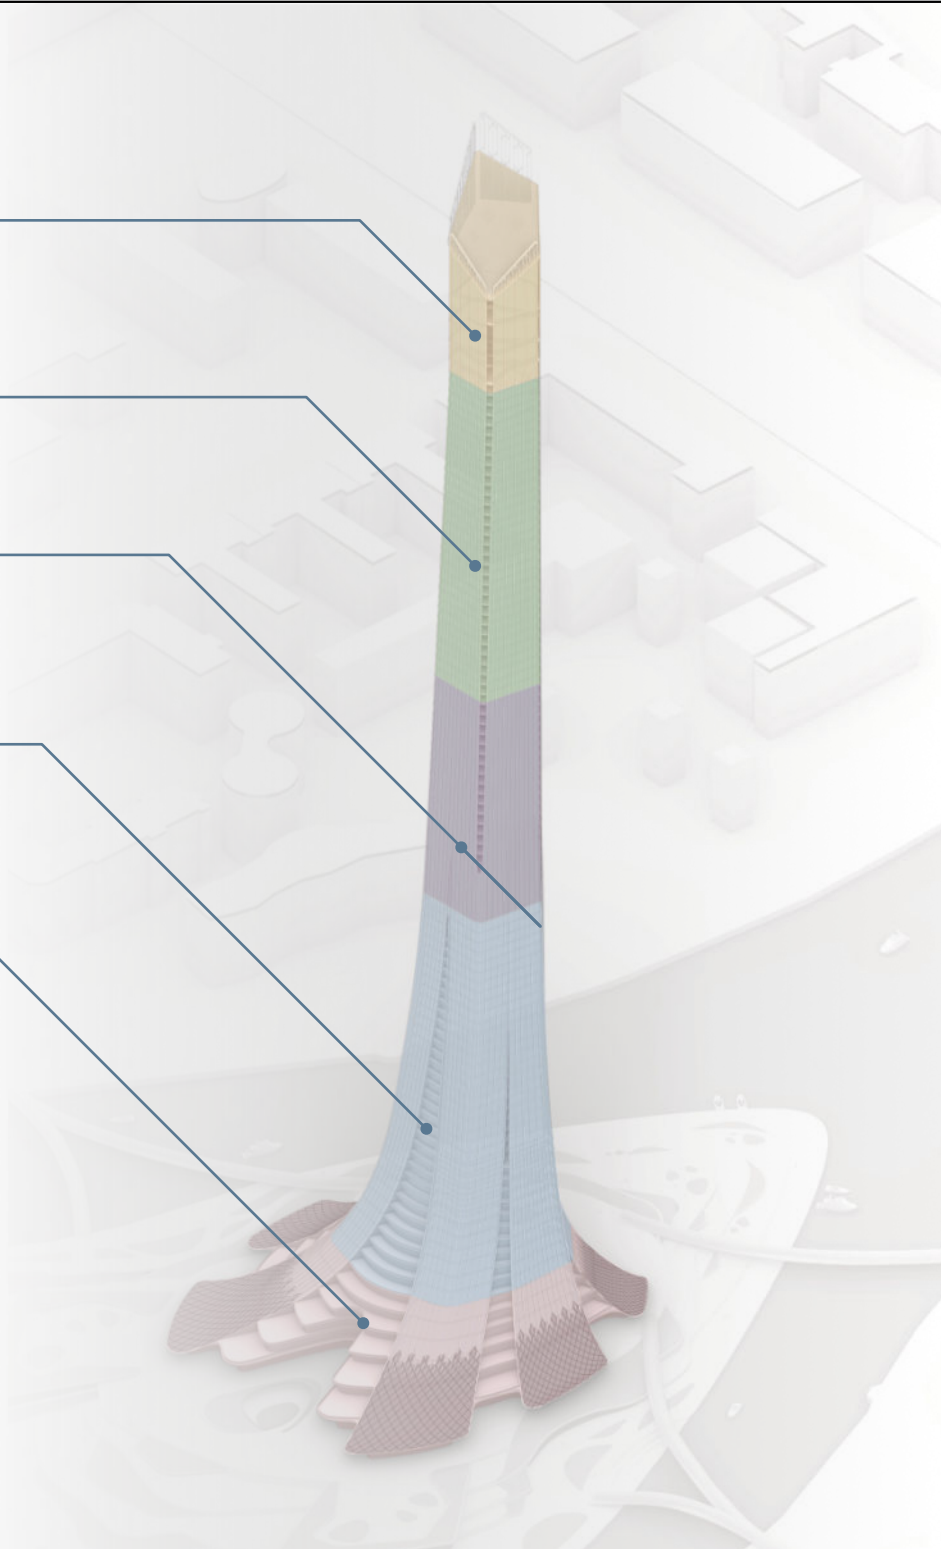

02 SEMEY MALL



PROJECT IDEA

The architectural expression is based on a simple and rational volumetric composition. The arrangement of the building volumes helps define public spaces, pedestrian connections, and visual corridors, strengthening the overall identity and legibility of the complex.



The facades incorporate transparent elements that create a strong visual connection between interior and exterior spaces, enhancing openness and interaction with the surrounding environment.

The main entrances are clearly emphasized, serving as key points of orientation for both pedestrians and arriving vehicles. Architectural elements are used not as decoration, but as functional tools that help communicate the building's structure and guide movement throughout the complex.

The building's spatial and planning framework is designed with flexibility in mind, allowing spaces to be adapted to changing needs over time. This ensures that the development remains relevant and functional not only today, but also in the long term.



SITE PLAN

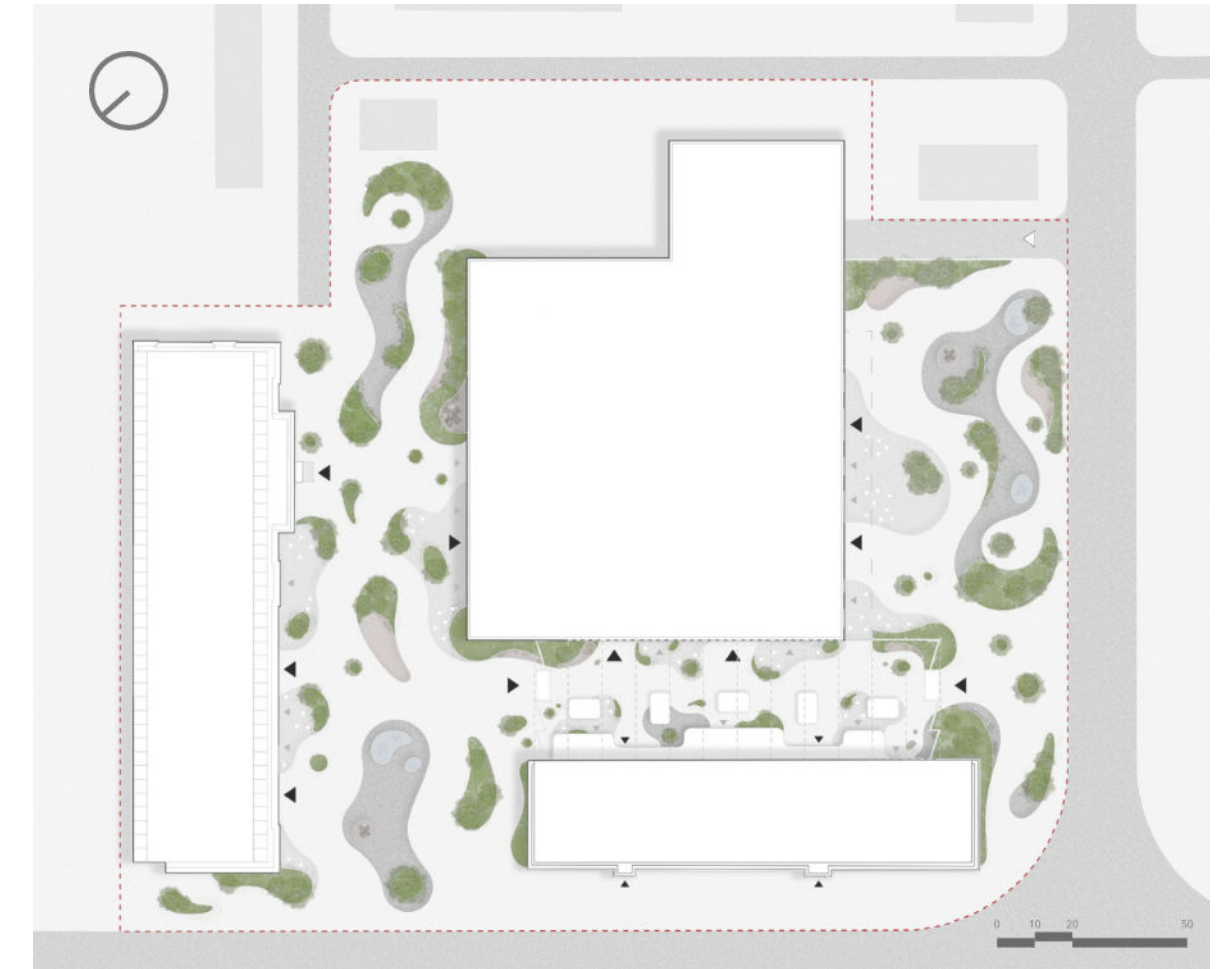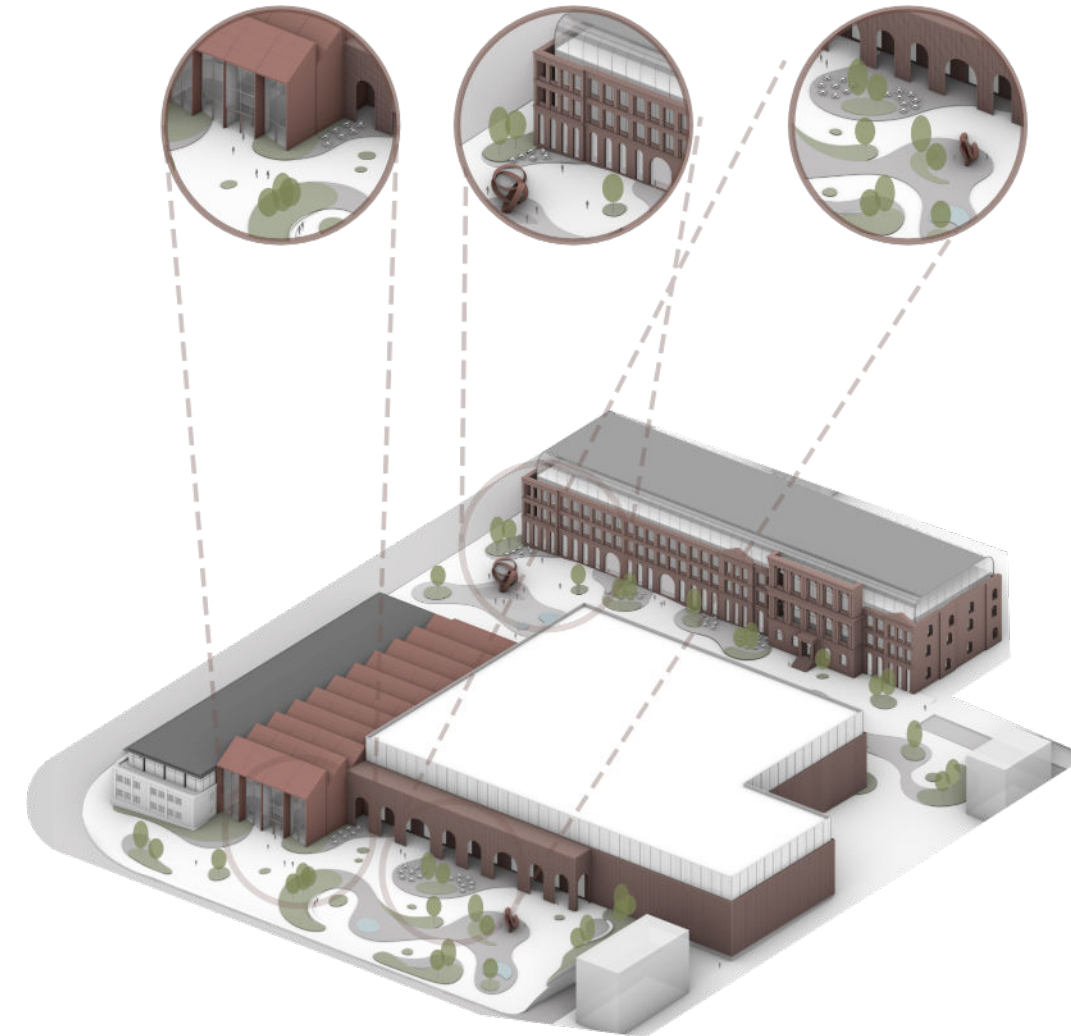

The site is organized around a clear functional zoning strategy and the separation of circulation flows. Buildings with different uses are positioned to create logical relationships between programs while ensuring smooth and intuitive movement throughout the development.

Primary visitor circulation is concentrated around clearly defined entrances and public spaces. From these points, movement naturally extends throughout the complex, allowing people to navigate between different areas without unnecessary repetition or dead ends. This creates a continuous and intuitive flow, which is particularly important for the commercial success of the development.

Transportation, service, and operational functions are organized separately from the main visitor routes. Logistics are located along the perimeter of the site, minimizing their impact on public spaces while ensuring the safe and efficient operation of the complex.

- site boundary
- building footprint
- ▲ main entrance
- ▲ secondary entrance
- △ entrance to underground parking and facilities



North - East facade



North - West facade



South - West facade




South - East facade

- Activity park ~ 4 325m²
- Businesscenter ~ 2 840 m²
- Corridors ~ 503 m²
- Vertical connections ~ 290 m²
- Restrooms ~ 130 m²

- Boutiques ~ 2 840 m²
- Electronics ~ 1 370 m²
- Commercial area ~ 4 220 m²
- Kids department ~ 1 860 m²
- Corridors ~ 1 960 m²
- Vertical connections ~ 380 m²
- Restrooms ~ 130 m²

- Supermarket ~ 2 730 m²
- Boutiques ~ 3 030 m²
- Mixed use ~ 2 980 m²
- Commercial area ~ 730 m²
- Restaurants ~ 1 830 m²
- Back of house ~ 500 m²
- Corridors ~ 1 968 m²
- Vertical connections ~ 380 m²
- Restrooms ~ 130 m²

- Commercial area ~ 3 600 m²
- Cinema ~ 2 230 m²
- Businesscenter ~ 2 840 m²
- Gym ~ 1 470 m²
- Gym reception ~ 360 m²
- Corridors ~ 1 178 m²
- Vertical connections ~ 364 m²
- Restrooms ~ 130 m²

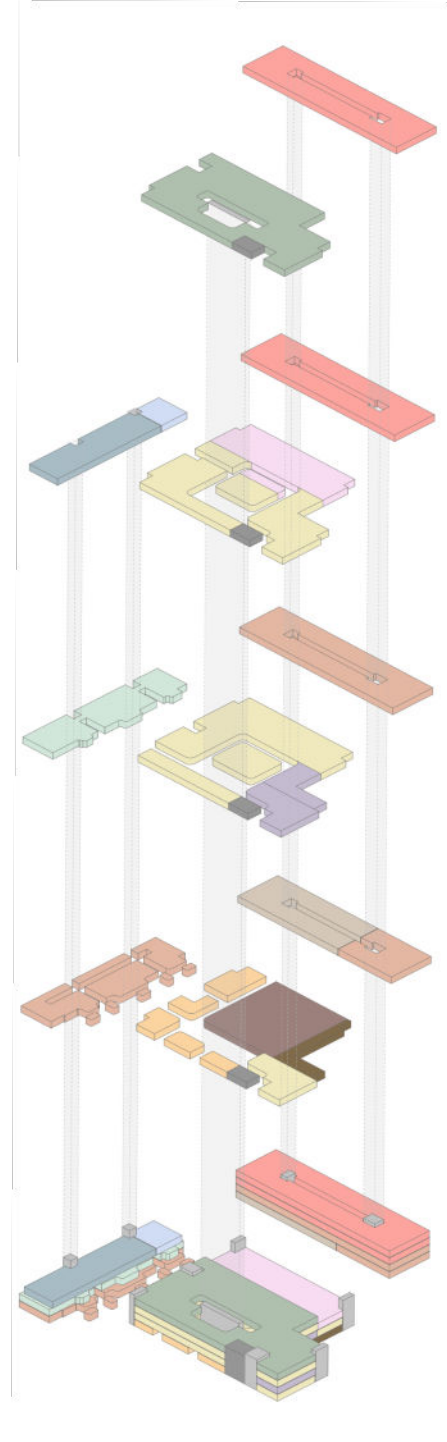


03

ETERNAL PEARLS


PROPOSAL FOR BUILDNER URBAN SCULPTURE COMPETITION



CONCEPT

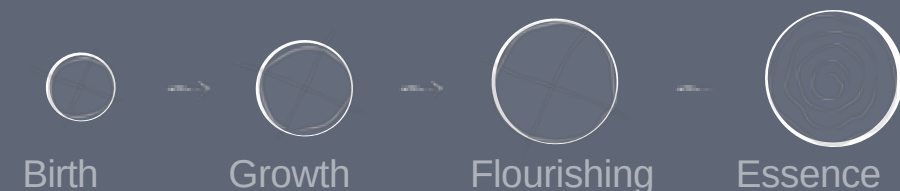

A wave rises from the sea, flowing across the shoreline and shaping the landscape. Its fluid form bends and undulates, creating elliptical depressions that cradle three pearls while also forming elevated pathways for visitors to explore and experience the surroundings. Within this wave, the pearls appear in different sizes, telling a story of growth, continuity, and transformation.

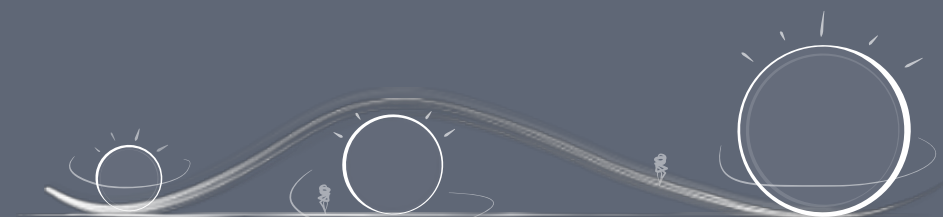


The smallest pearl, positioned closest to the sea, represents the past—the beginning of the journey. It honors the nation's roots and its rich pearl-diving heritage.


The middle pearl flourishes within the wave, embodying the present: prosperity, resilience, and growth amid challenges, much like an oasis thriving in the desert.

The largest pearl, oriented toward the city, rises toward the sky and symbolizes the future—ambition, innovation, and limitless potential. It reflects a vision of continuous progress and evolution.

Together, the wave and the pearls create a symbolic journey from sea to city, from past to future, inviting visitors to experience the sculpture from multiple perspectives and discover new meanings along the way.

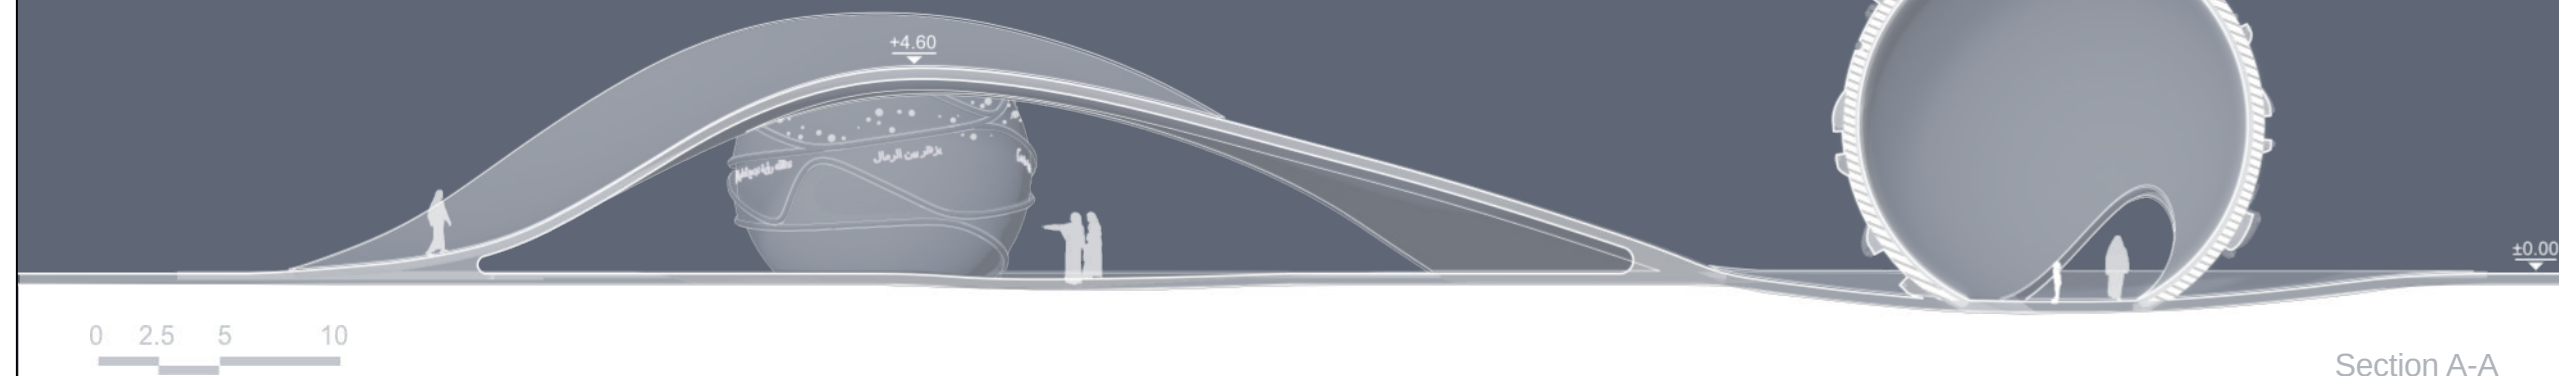

Section A-A

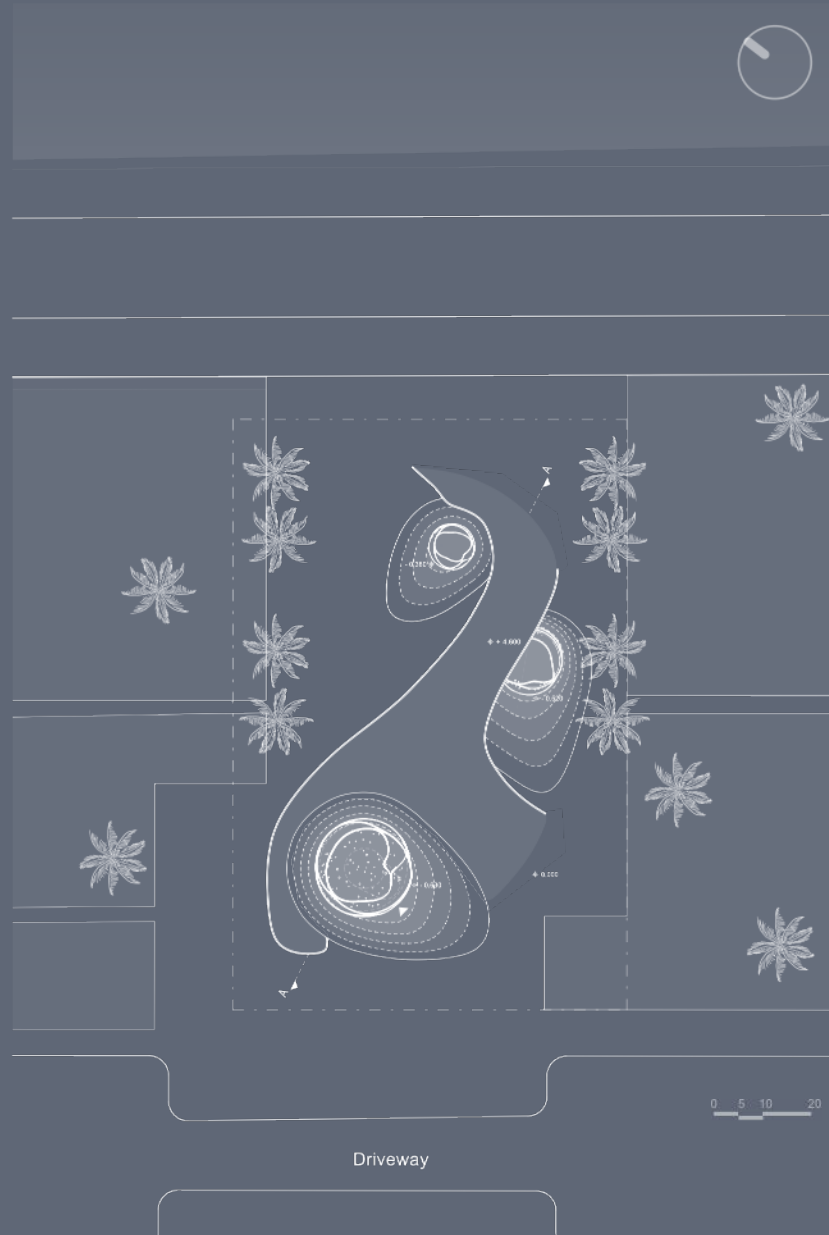

Along the eastern coast of Al Khobar, on the shores of the Arabian Gulf, life was once deeply connected to the sea. Long before the discovery of oil, generations of pearl divers ventured into its waters in search of treasures hidden within oyster shells—gems that demanded courage, patience, and perseverance to find.

These pearls were more than valuable goods. They symbolized survival, heritage, and the early aspirations of the nation. The pearl-diving tradition shaped not only the economy but also the culture, identity, and stories of coastal communities.

It is from this rich history that the inspiration for our sculpture emerges.



North - East facade



South - West facade



04

ACADEMIC PROJECT

URBAN BLOCK
PROPOSAL

2024



MASTER PLAN

The proposed site is located at the intersection of two Vilnius districts – Šnipiškės and Šeškinė. The area is currently occupied by a shopping center and a large surface parking lot. The redevelopment envisions a mixed-use urban quarter that not only responds to the needs of local residents but also serves as a statement of contemporary sustainability principles. These principles extend beyond design and material choices, aiming to encourage more sustainable lifestyles and habits among residents and visitors.

To protect the site from noise and air pollution, perimeter buildings are proposed along the busy Žalgirio and Geležinio Vilko streets. Building heights gradually increase from the intersection of these two streets, responding to the surrounding urban context. The main buildings accommodate public, office, and commercial functions, while residential buildings are located within the quieter inner part of the quarter. Varying building heights create a dynamic urban composition, while underground parking allows more space to be dedicated to public areas.

The site is adjacent to the Neris Oxbow Park, the Japanese Garden, and the Šeškinė Slopes Nature Reserve. As a result, natural elements are integrated throughout the development and into the building façades. Proposed sustainability features include green façade systems, rainwater collection solutions, and solar energy installations.

The architectural character combines industrial and commercial influences, which come together most prominently in the theatre building. Views into the green heart of the quarter are visible from the main streets, inviting visitors to explore further. The interior of the development features a variety of public spaces, including a commercial promenade, a youth plaza, and an open pond surrounded by recreation, play, and sports areas.

The project aims to create a vibrant, sustainable, and multifunctional urban environment that will become a new destination for residents and visitors between the Šnipiškės and Šeškinė districts.



SITE PLAN

The site plan is designed to clearly separate different circulation flows while creating a protected residential environment shielded from the impact of heavy traffic.

The development is composed of several building groups arranged in perimeter and semi-perimeter formations, defining a series of communal inner courtyards and shared outdoor spaces.

The key element of the spatial layout is the network of internal courtyards, where pedestrian paths and green spaces create clear yet fluid connections between buildings. An X-shaped pathway system naturally draws residents toward the central open space, which serves as the heart of everyday community life.

Transportation infrastructure is organized through a clear hierarchy of movement. Vehicle circulation and parking are concentrated along the perimeter of the site, minimizing their impact on internal spaces, while pedestrian and bicycle routes are integrated into a network of green corridors. This approach helps maintain a calm, safe, and human-scaled environment throughout the development.

Green spaces and permeable landscape surfaces are treated not only as aesthetic features but also as key structural elements of the masterplan. They break down the scale of the built environment, create comfortable microclimates, and provide the site with openness and room to breathe.

